



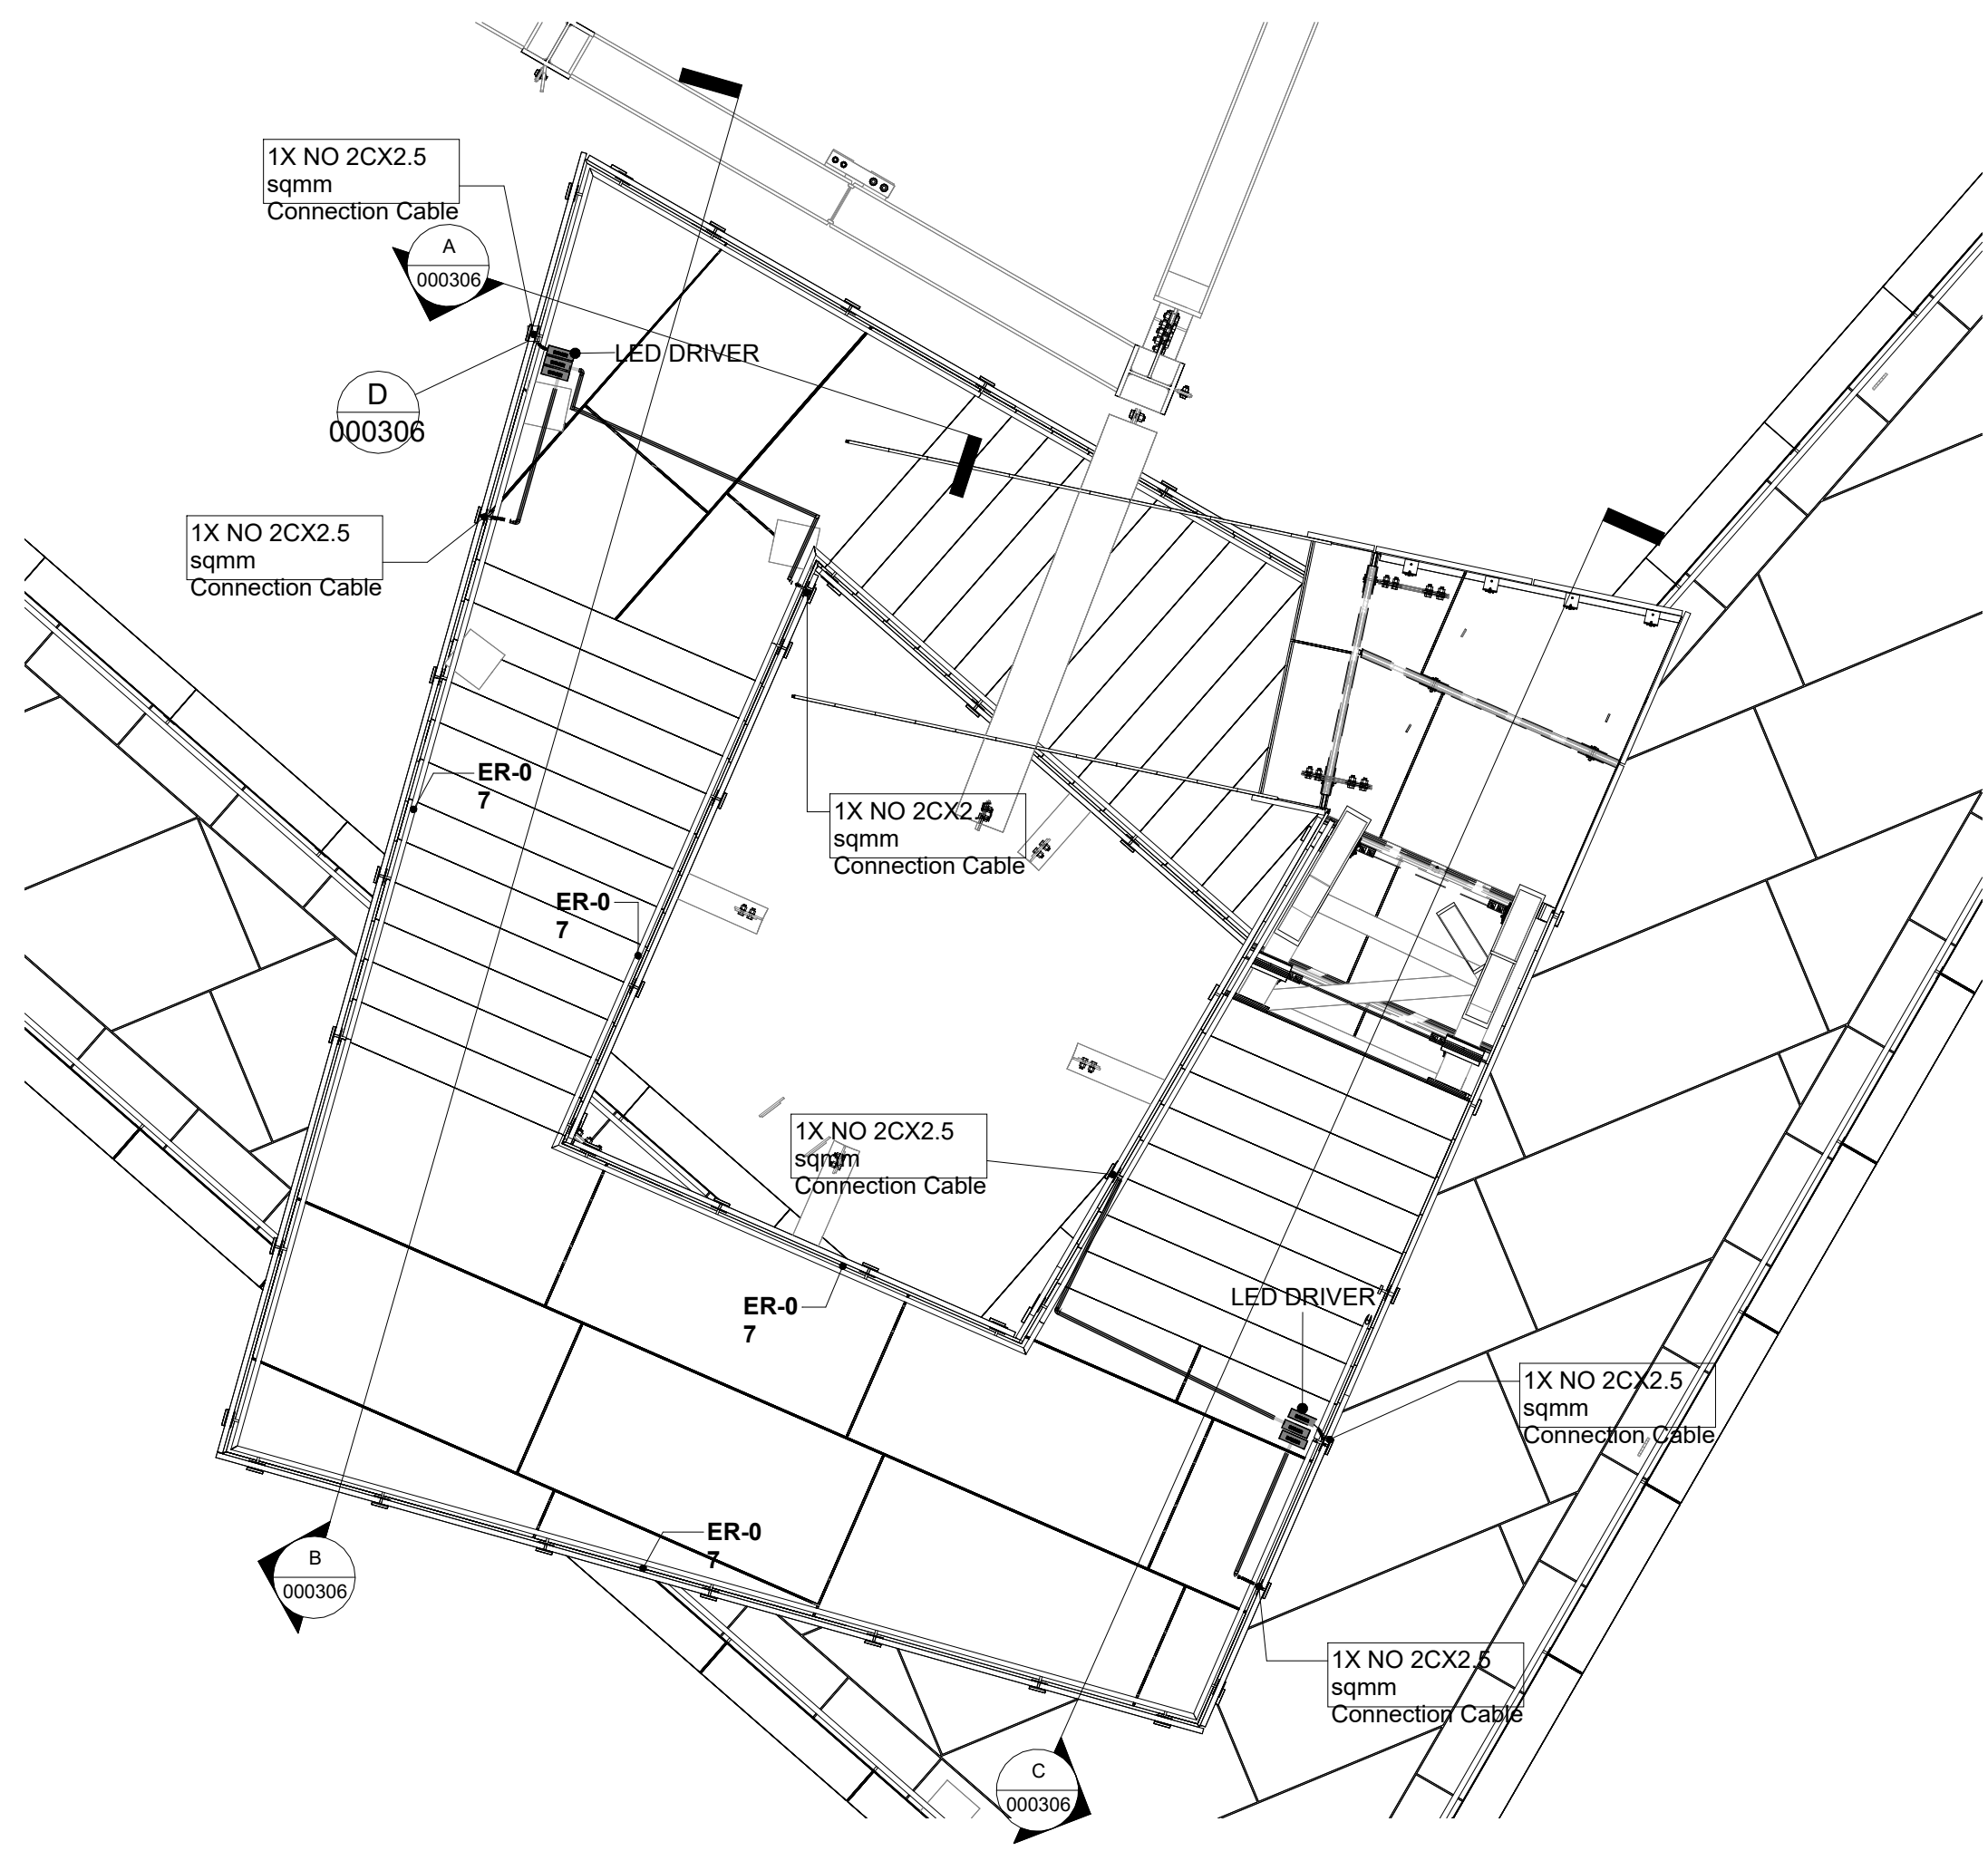


1 STAIR AU Level 02
1 : 50

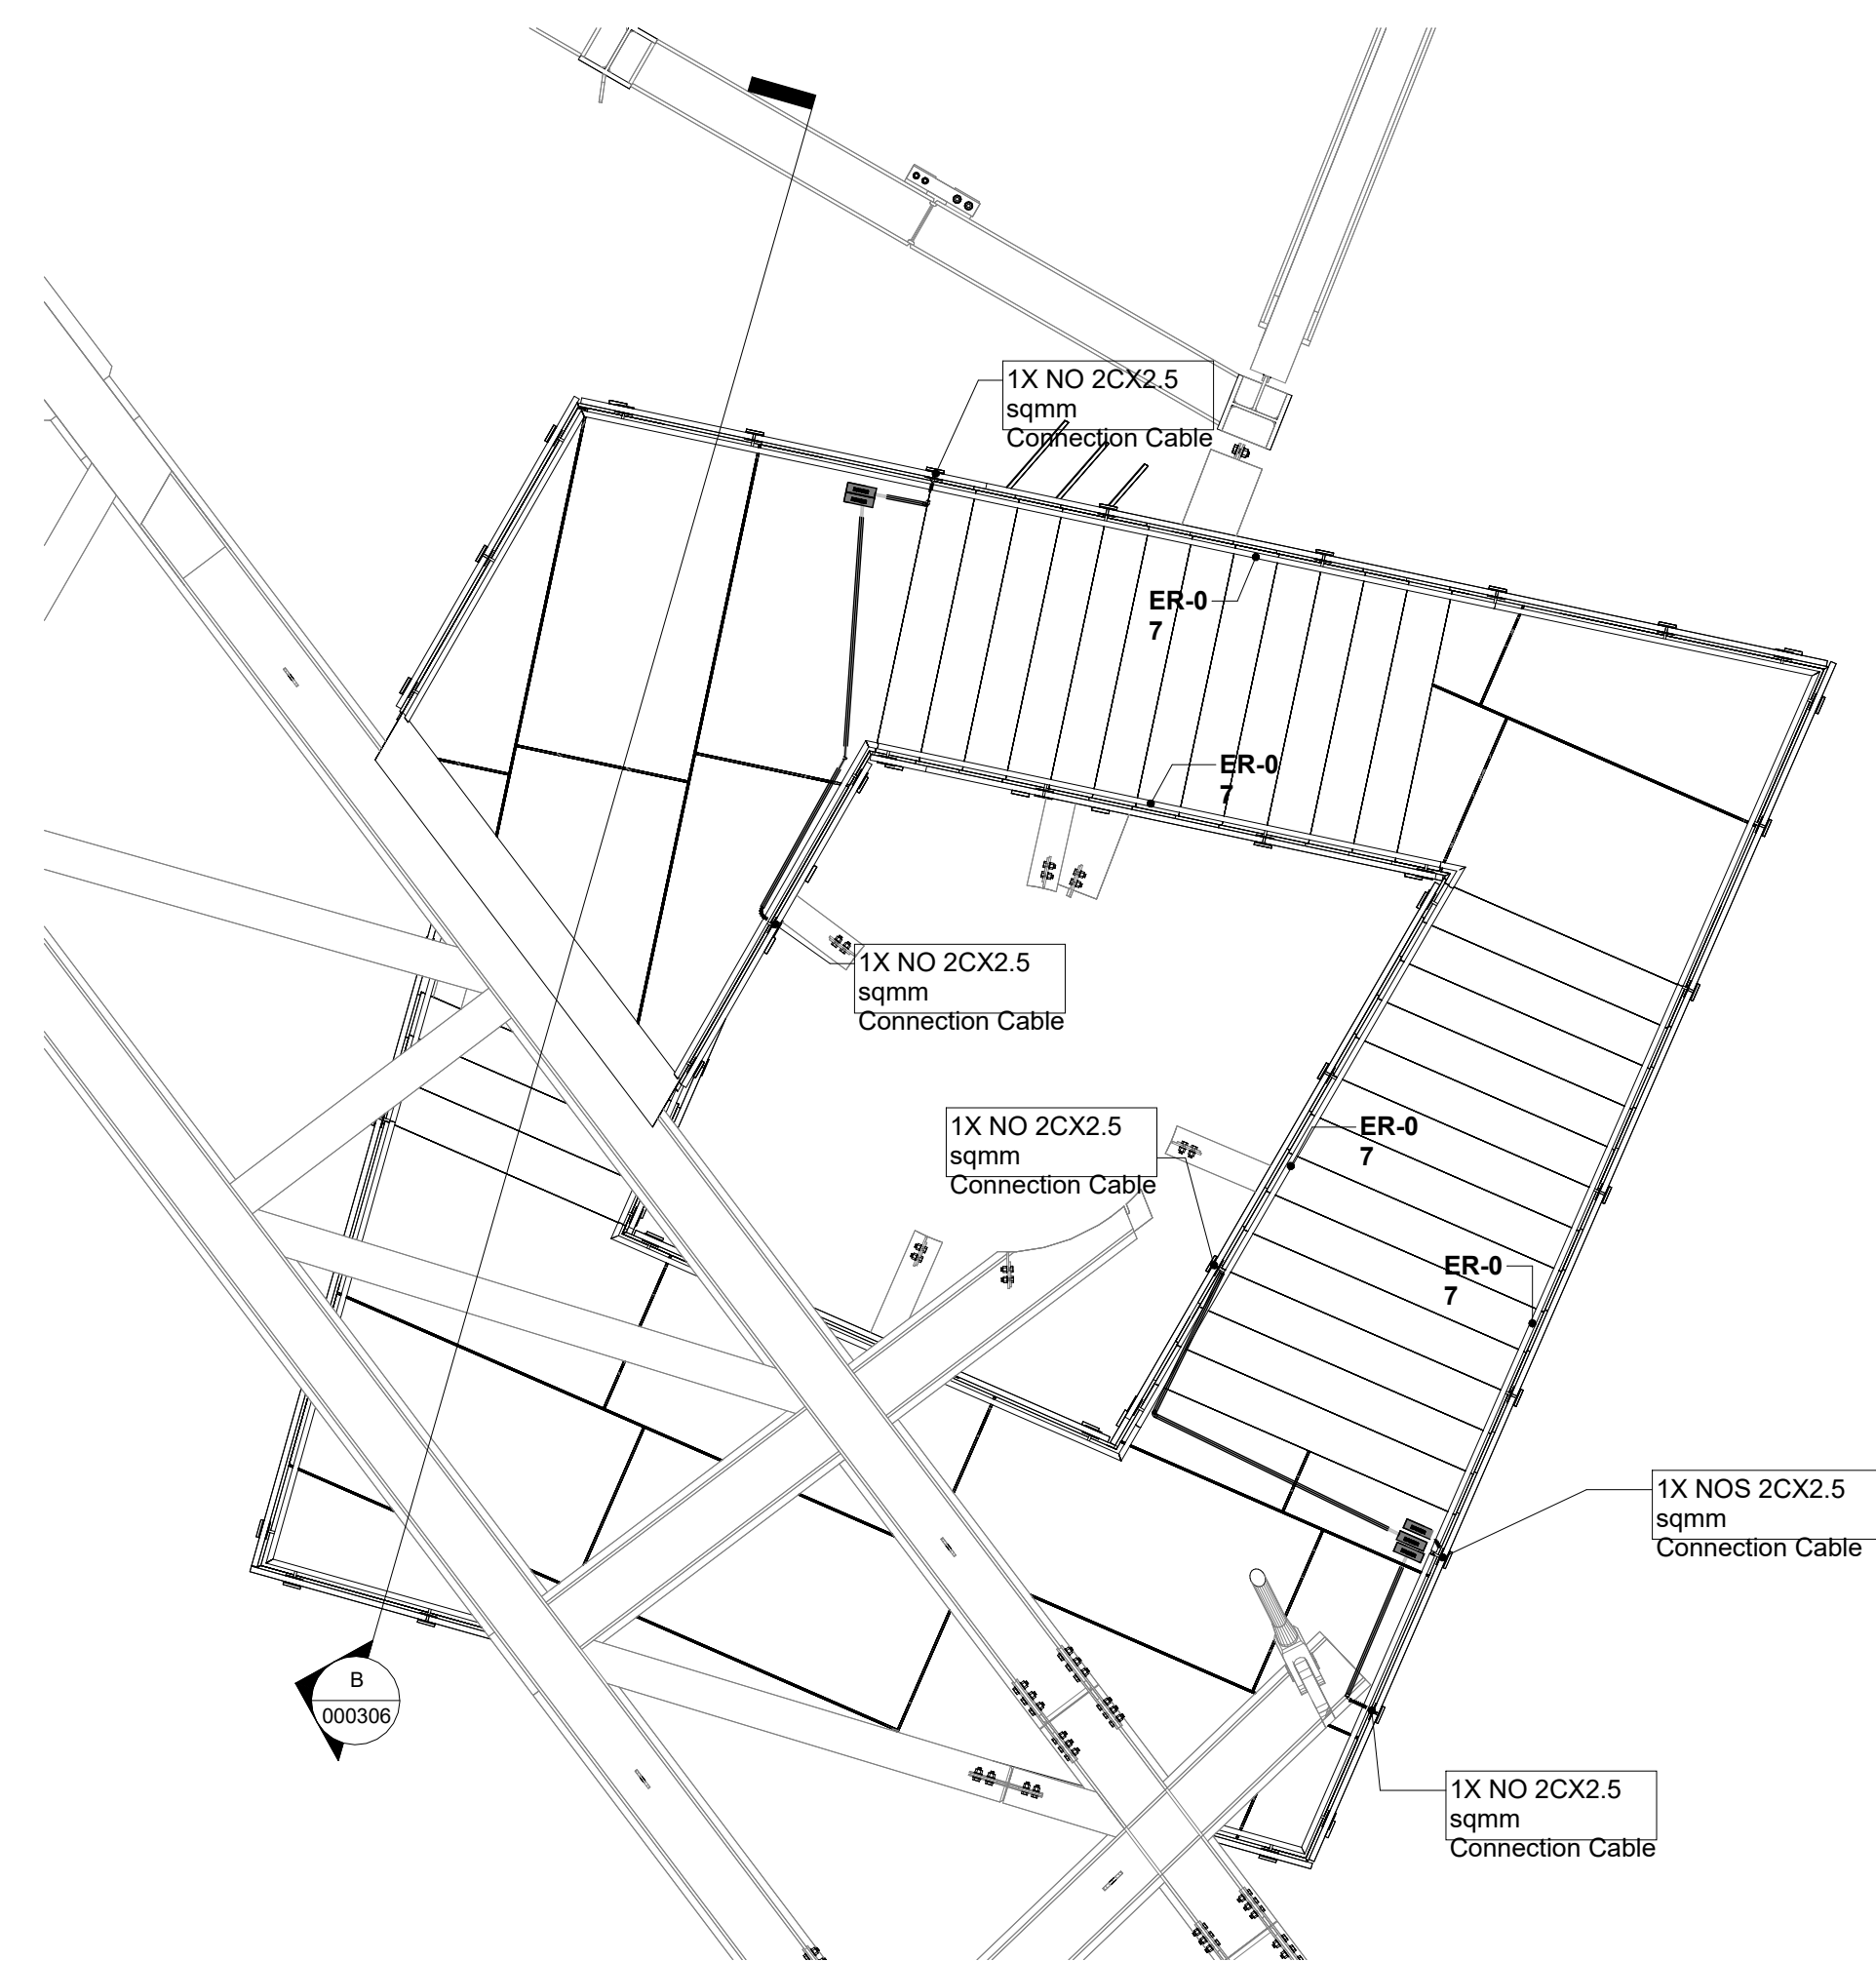

2 STAIR AU MEZZANINE 02
1 : 50


02_Mezzanine 02
32000.00n +32.000 m

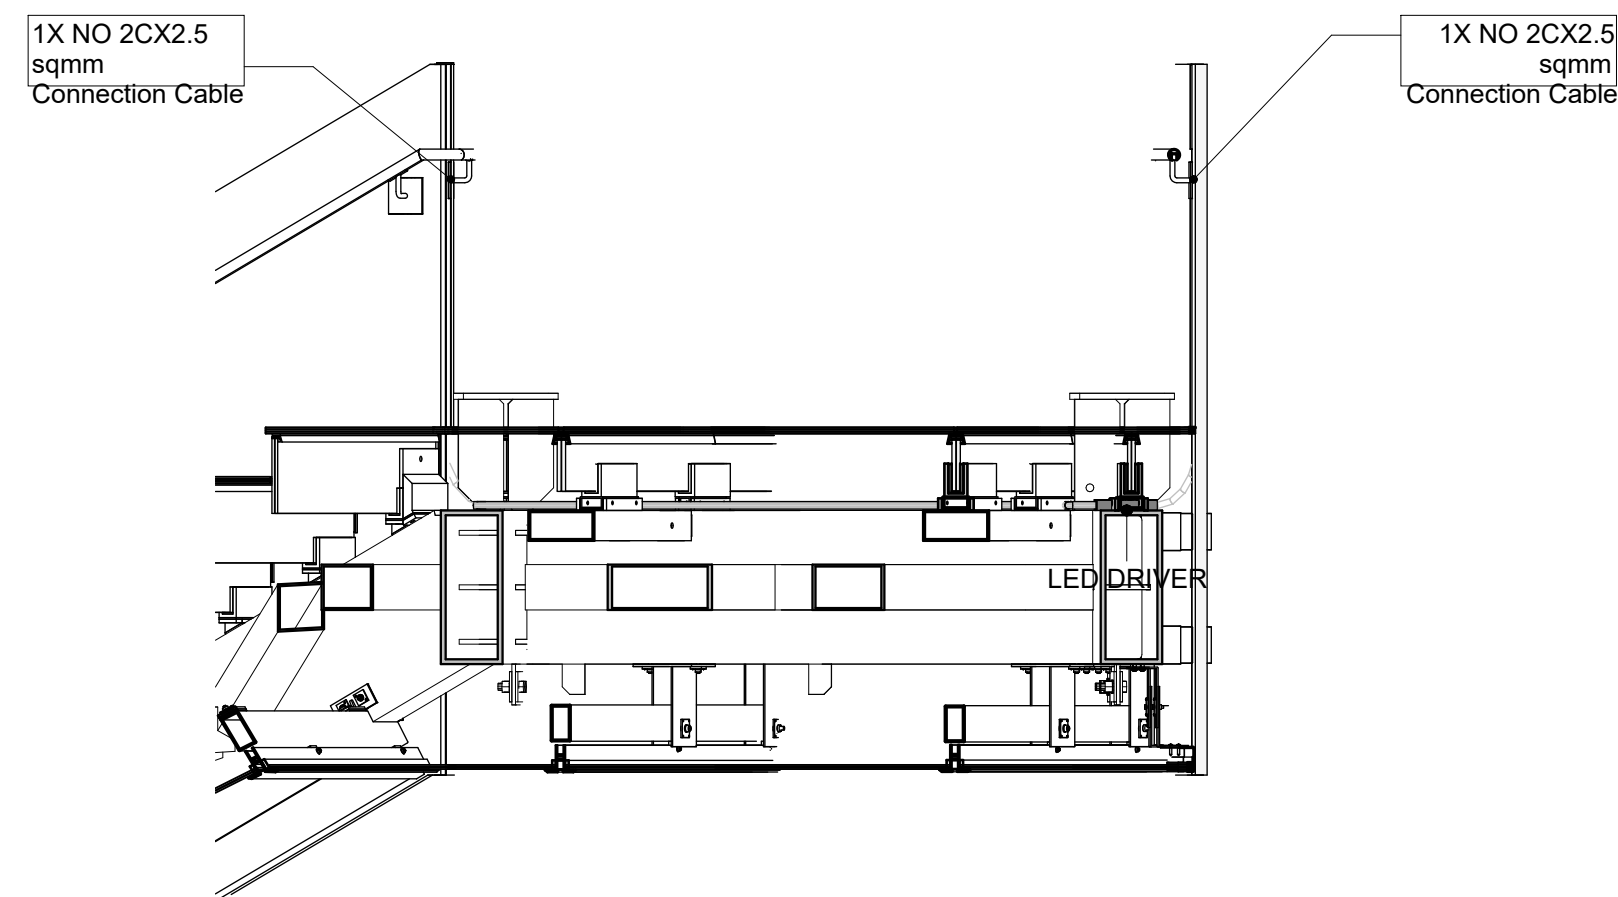


A STAIR AU - SECTION A
1 : 25

02_Level 02
27500.00n +27.500 m

02_Mezzanine 02
32000.00n

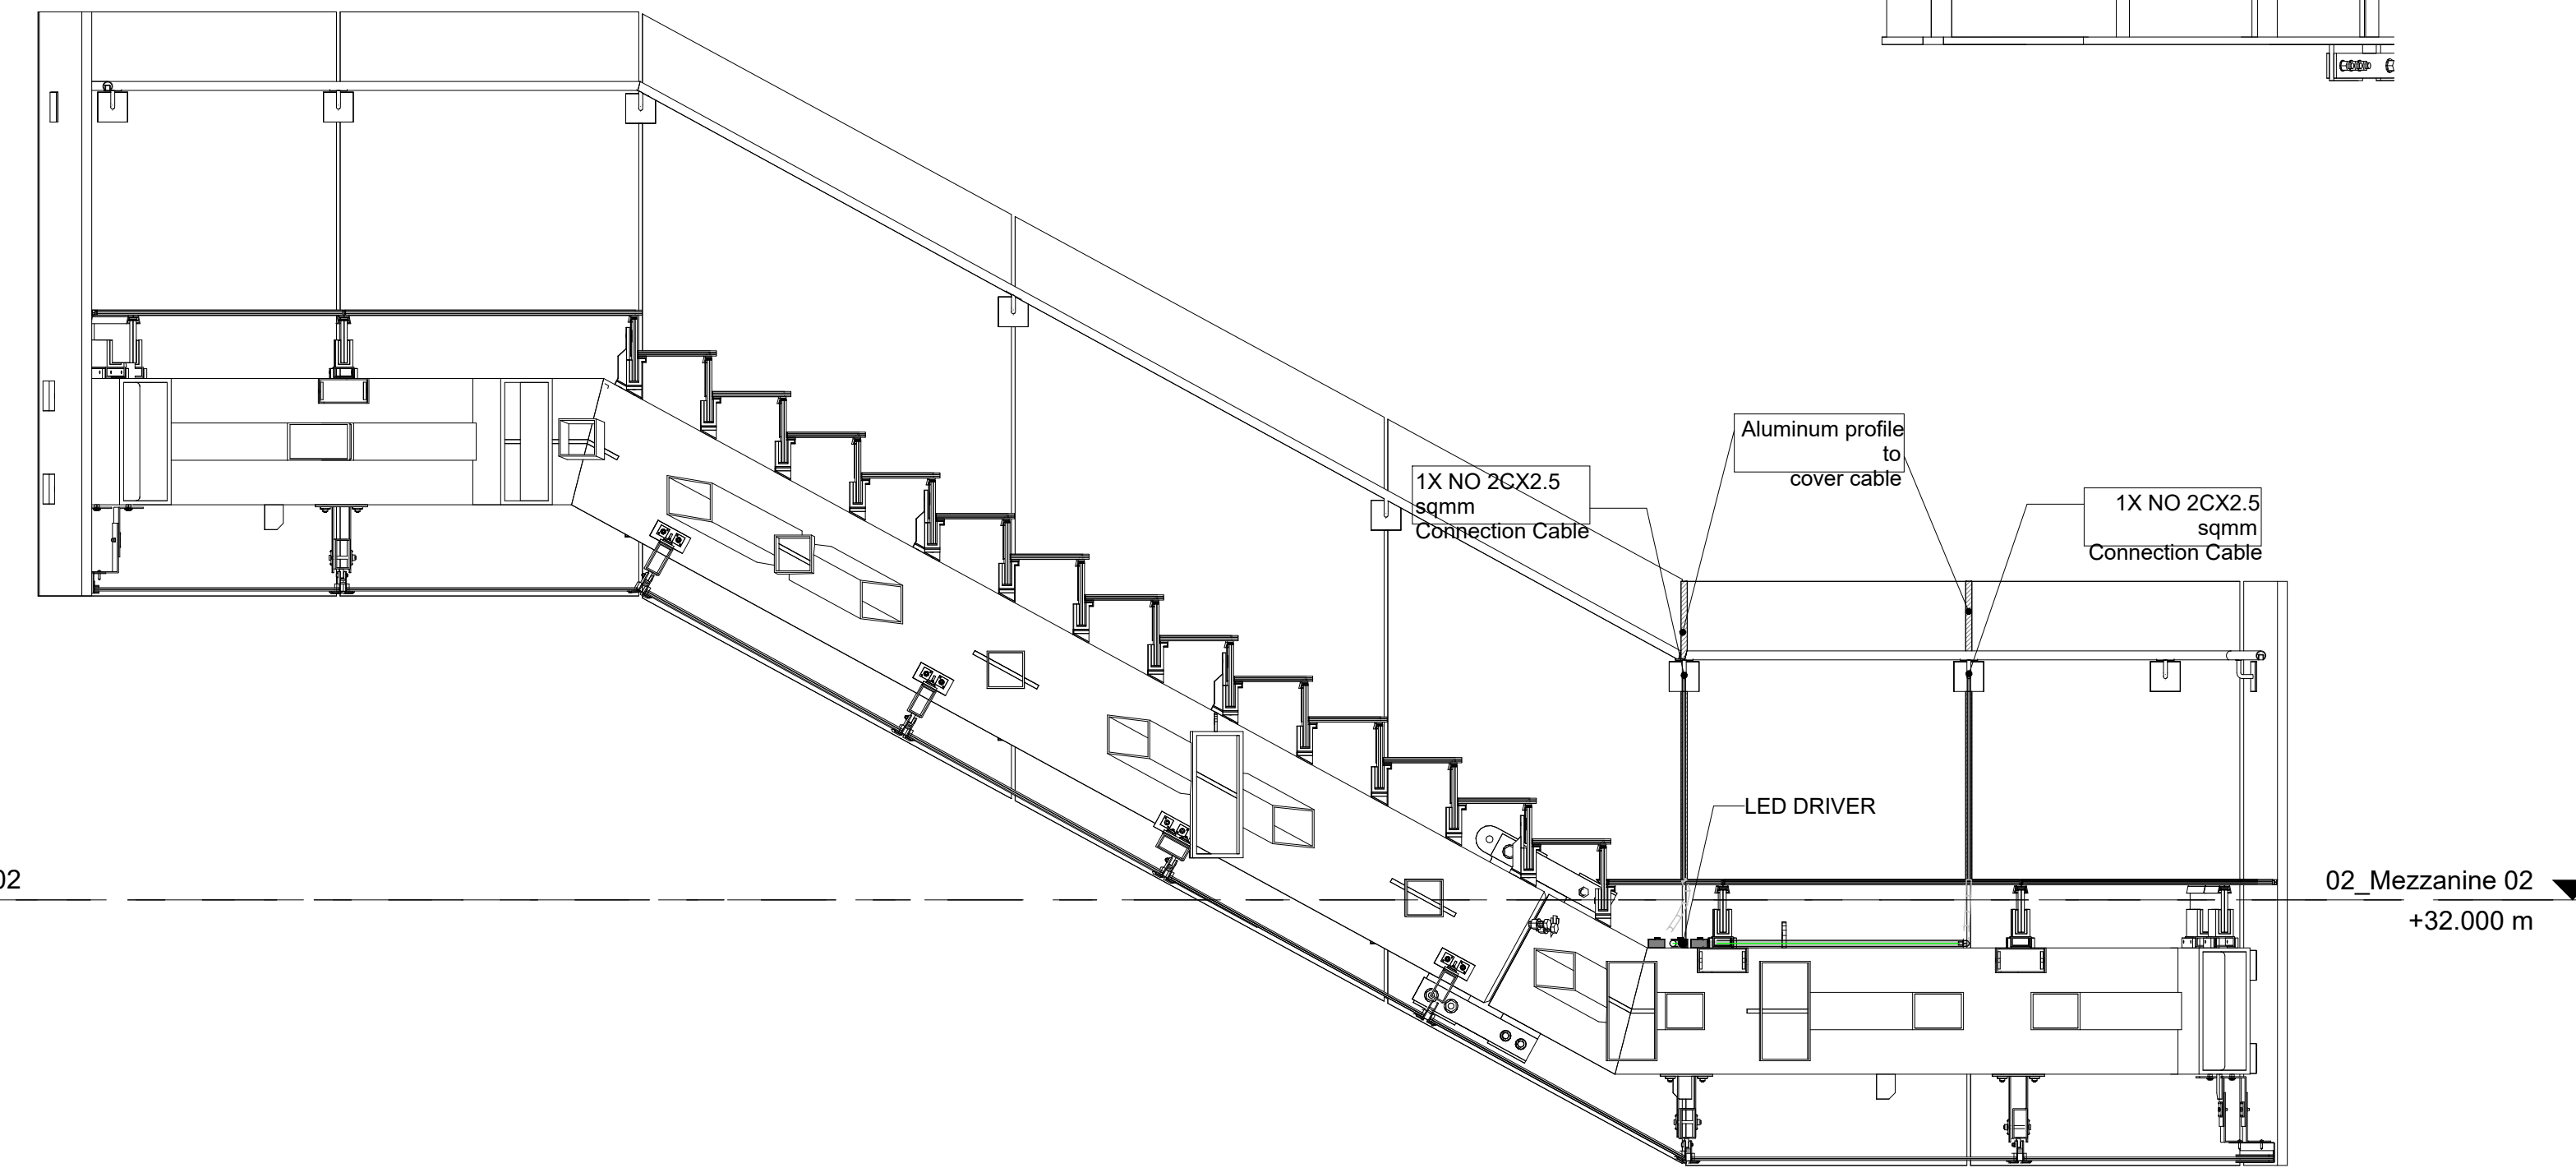


C STAIR AU - SECTION C
1 : 25

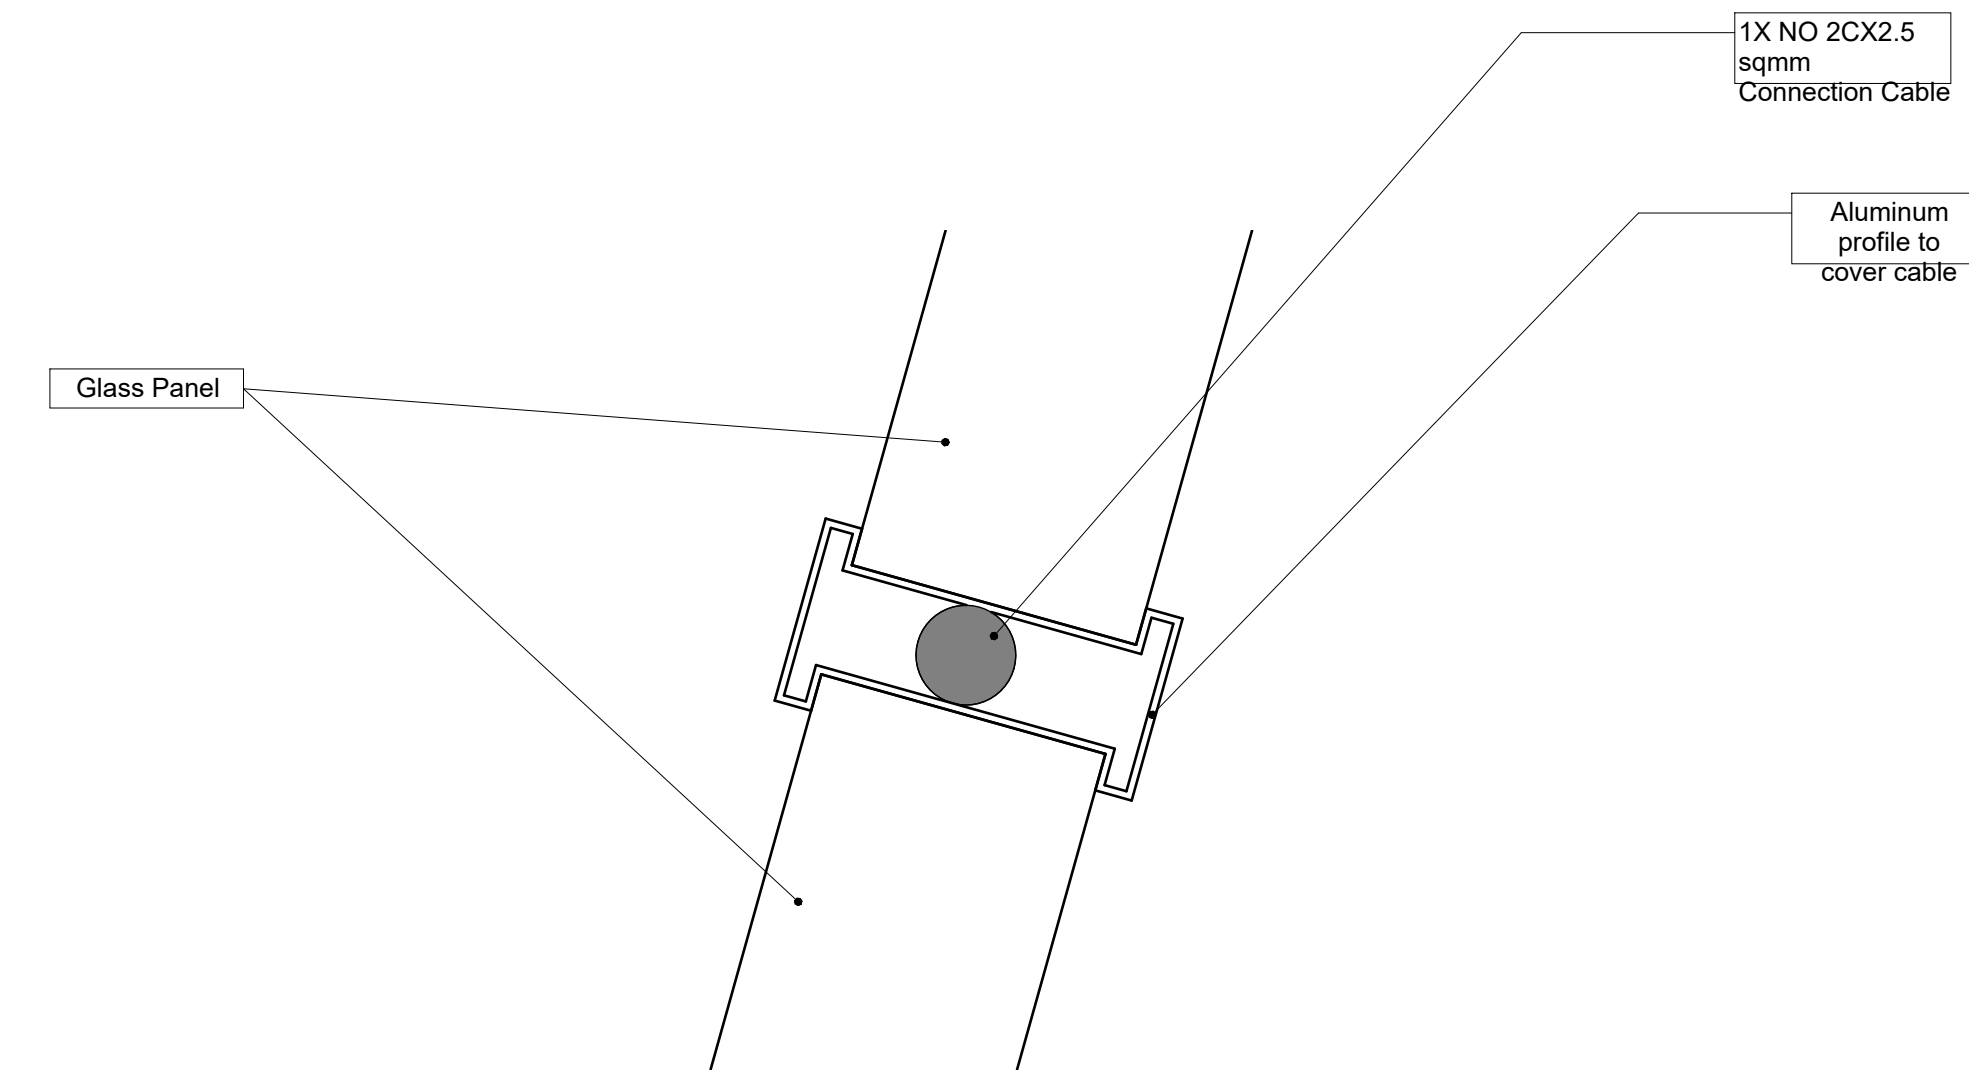

D STAIR AU - WIRE CONNECTION
1 : 1


02_Mezzanine 02
32000 mm

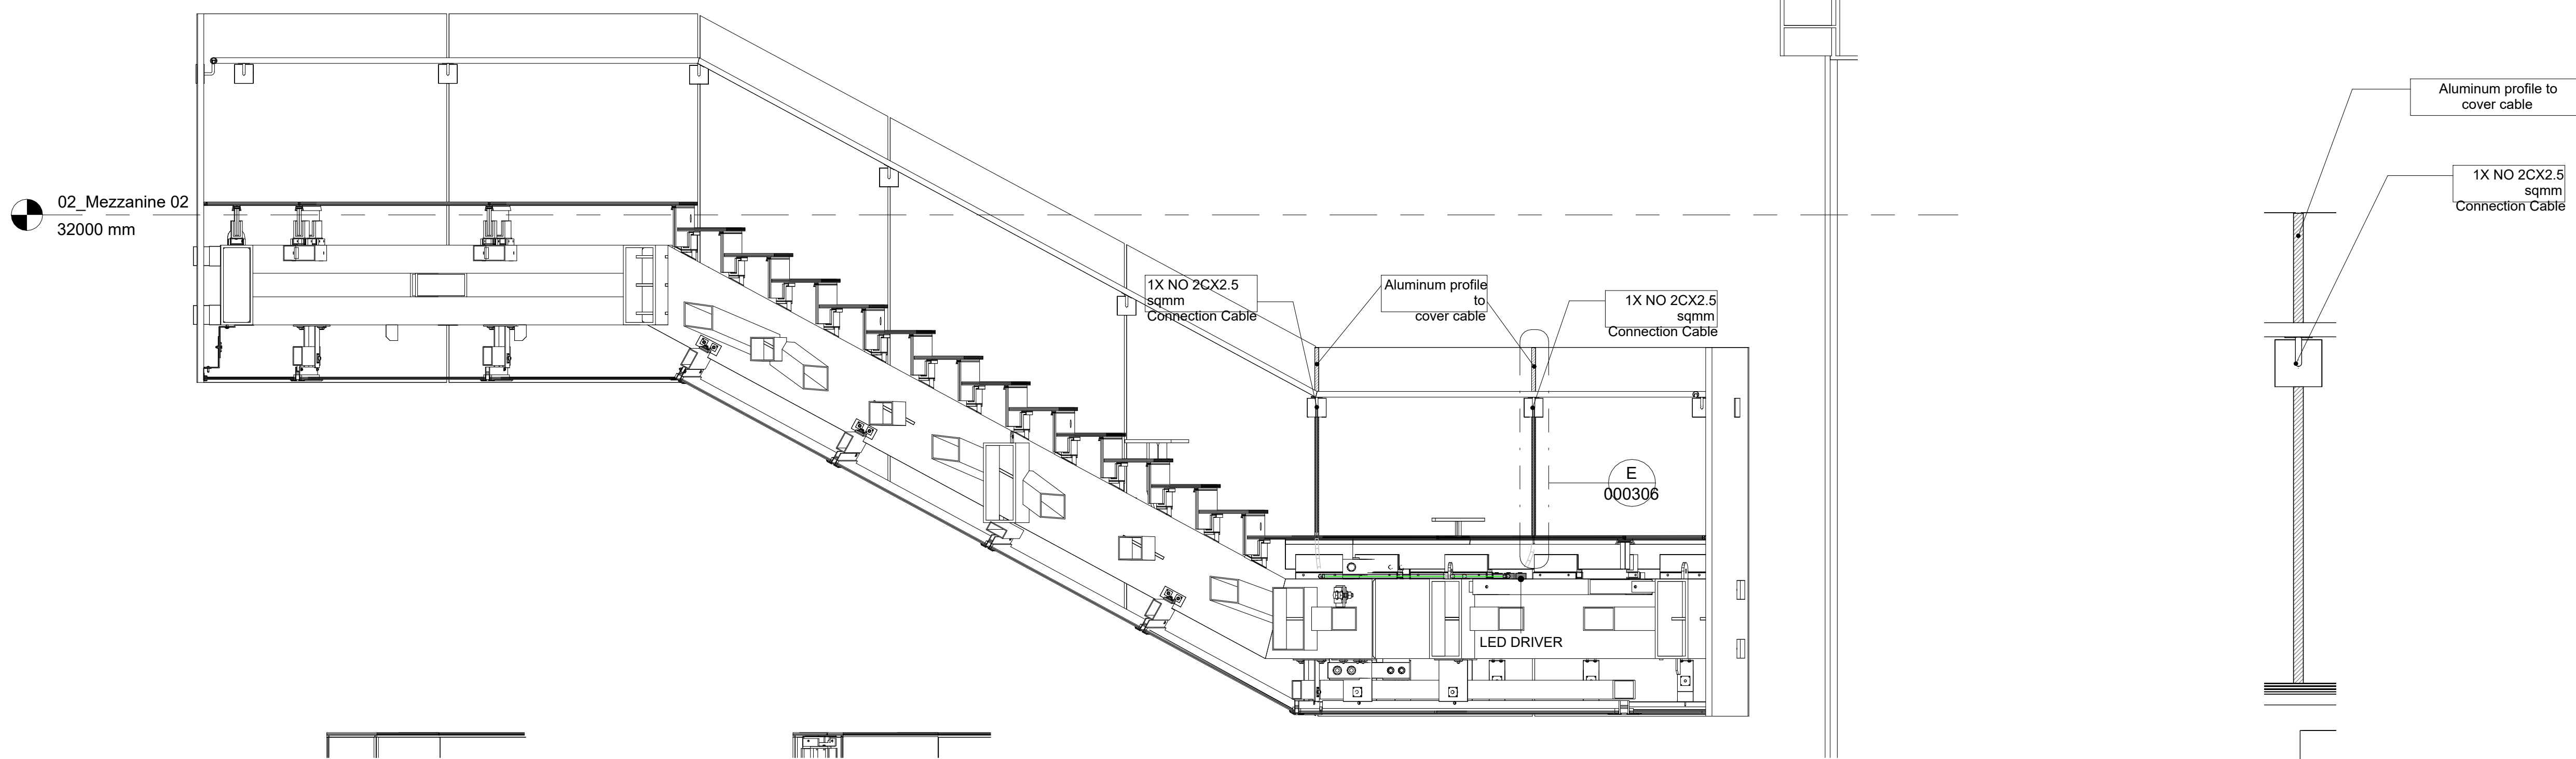

B STAIR AU - SECTION B
1 : 25

E STAIR AU - WIRE CONNECTION B/W GLASS
1 : 10

KEY PLAN

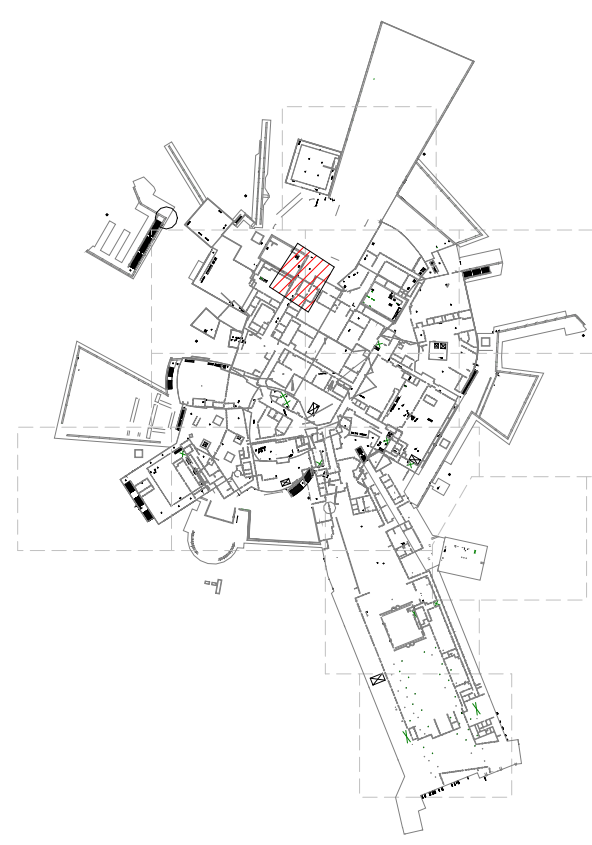

GENERAL NOTES:
1. ALL DIMENSIONS ARE IN MILLIMETERS AND LEVELS ARE IN METER (MAD) UNLESS NOTED OTHERWISE.
2. DO NOT SCALE FROM THIS DRAWING. ONLY WRITTEN DIMENSIONS ARE TO BE FOLLOWED.
3. ANCHORAGE LENGTH AS PER STRUCTURAL PARTIAL MAT SLAB PLAN ZONE.
4. DRAWINGS: DT-5-12-20 Rev 01
5. CLIENT REFERENCE: DRAWING NUMBER:
REVIT MODEL LINKS REFERENCE:
GAD-STFG-HGL-PJW-STW-MOD-000005.rvt
GAD-STFG-HGL-PJW-STW-MOD-000009.rvt
GAD-STFAB-ELC-PJW-203-MOD-000005.rvt
GAD-STES-SST-ATM-STW-MOD-000002.rvt

MATERIAL SUBMITTAL REFERENCE:
GAD-ST-AV-MAS-ARC-00121
CALCULATION SUBMITTAL REFERENCE:
GAD-STSL-CAL-ARC-000002

SHEET MODEL REFERENCE: GAD-STSL-ARC-PJW-MOD-000001

NO.	FOR APPROVAL	DATE	SS	ARC	UP
19	19-03-2025	SS	ARC	UP	

PROJECT OWNER

دائرة الثقافة والسياحة
**DEPARTMENT OF
CULTURE AND
TOURISM**

PROJECT MANAGER
**TURNER CONSTRUCTION
-INTERNATIONAL LLC**
P.O. BOX 880, ABU DHABI, UAE
TEL: +971 2 8500 888

CONSULTANTS
GEHRY PARTNERS, LLP.
ARCHITECT
12541 BEATRICE STREET LOS ANGELES, CALIFORNIA 90066 USA
TEL: 310-480-3000
ARUP
ENGINEER
900 WILSHIRE BLVD., 19TH FLOOR LOS ANGELES, CALIFORNIA 90017 USA
TEL: 310-578-4400

CONSULTANT OF RECORD
ARUP GULF LTD
12TH FLOOR,
ABU DHABI UNIVERSITY TOWER,
AL MURQOR STREET,
PO BOX 18601
ABU DHABI, UNITED ARAB
EMIRATES
SUPERVISION CONSULTANT
PARSONS BRINCKERHOFF LTD
ABU DHABI
A MEMBER OF THE HSP GROUP
P.O. BOX 44746, SKY TOWER, LEVEL 36
OFFICE UNIT 3602, REEM ISLAND, ABU DHABI, UAE
TEL: +971 2 658 9226 FAX: +971 2 657 8772

MAIN CONTRACTOR
سكس كونستراكت
Six Construct **TROJAN**
GENERAL CONTRACTING

SUB CONTRACTOR
Spectrum Lighting Technology LLC
Dubai Investment Park II,
P.O. 54563, Dubai, UAE.
Tel: +971 4 80 80 507
e-mail: info@spectrumllc.com

PROJECT NAME
GUGGENHEIM ABU DHABI

ZONE
CULTURAL DISTRICT, SAADIYAT ISLAND

SECTOR NO.
SDN1
PLOT NO.
P7

**MODERN AND CONTEMPORARY
ART MUSEUM**

DRAWING TITLE
STAIR AU LED LIGHTING LAYOUT

DRAWING NUMBER
GAD-STSL-ARC-PJW-STW-DWG-000306
REVISION NO.
00

DATE
19-03-2025
SCALE
As indicated

ACM PROJECT NUMBER:
B1N-2018-005679

OFFICIAL USE ONLY